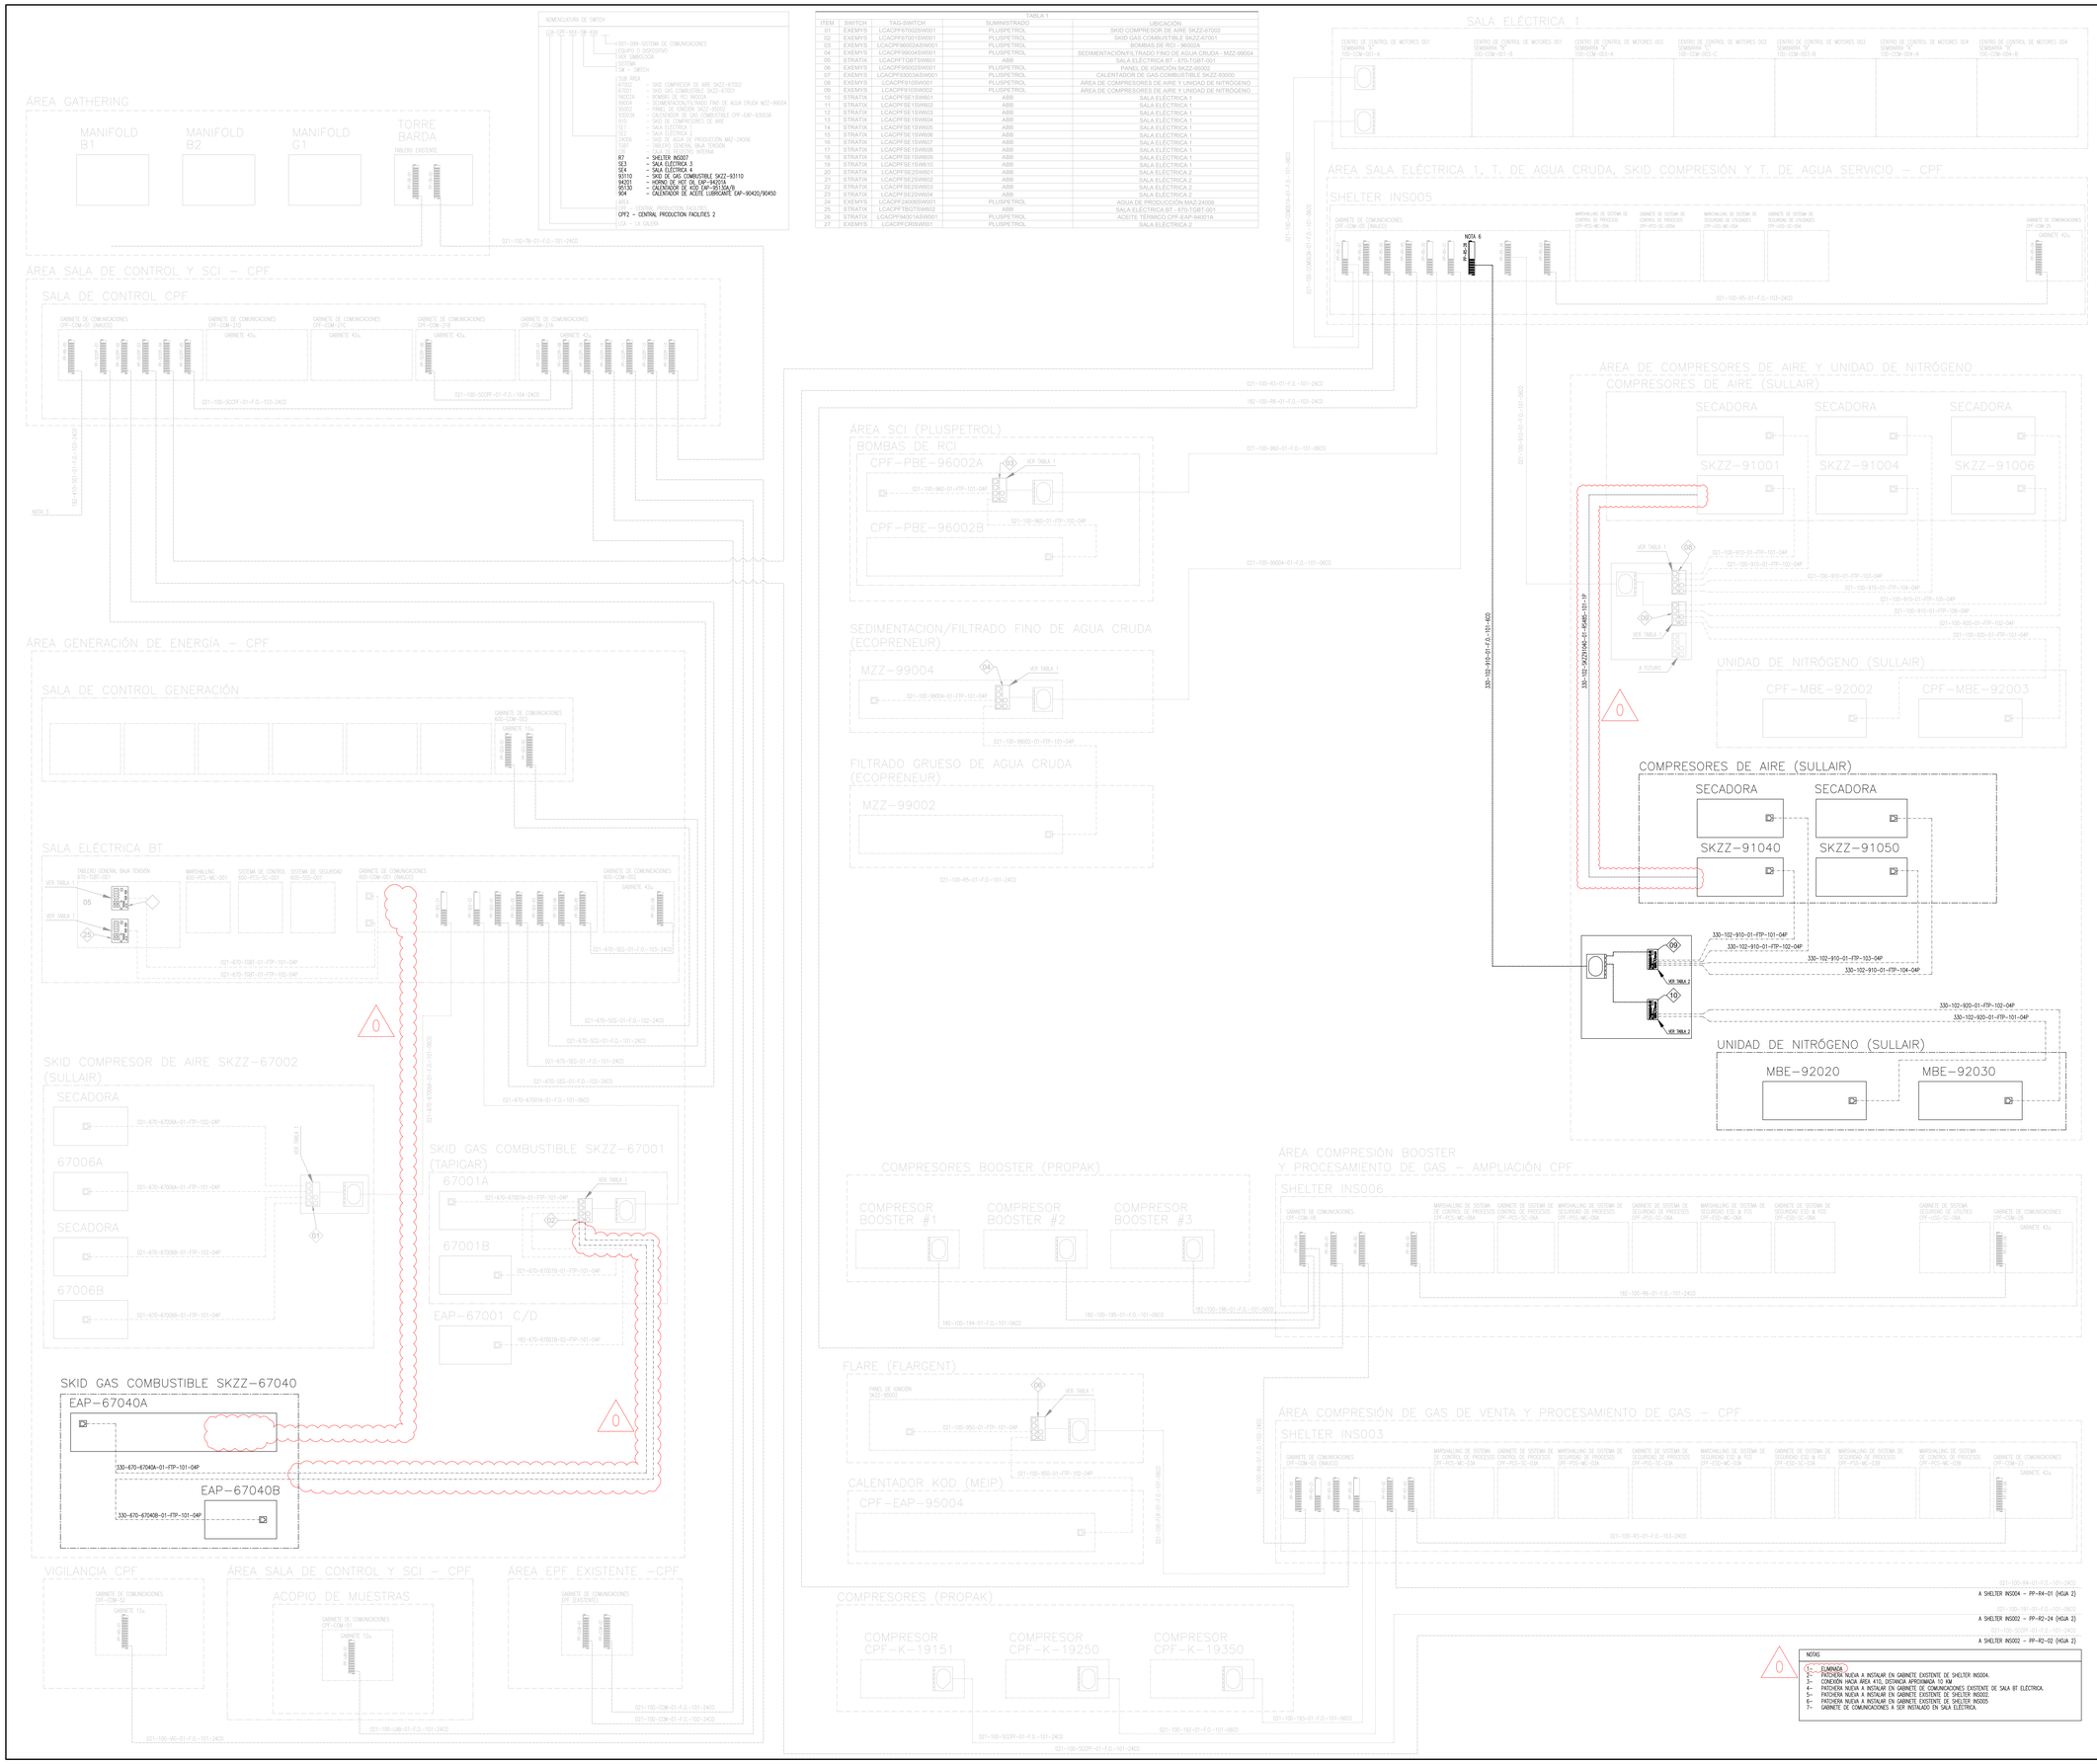

TABLA 1				
ITEM	SWITCH	TAG-SWITCH	SUMINISTRADO	UBICACIÓN
01	EXEMYS	LCACPF67002SW001	PLUSPETROL	SKID COMPRESOR DE AIRE SKZZ-67002
02	EXEMYS	LCACPF67001SW001	PLUSPETROL	SKID GAS COMBUSTIBLE SKZZ-67001
03	EXEMYS	LCACPF96002SW001	PLUSPETROL	BOMBAS DE RCI - 96002A
04	EXEMYS	LCACPF99004SW001	PLUSPETROL	SEDIMENTACIÓN/FILTRADO FINO DE AGUA CRUDA - MZZ-99004
05	STRATIX	LCACPF15BT0W601	ABB	SALA ELÉCTRICA BT - 670-TGBT-001
06	EXEMYS	LCACPF99002SW001	PLUSPETROL	PANEL DE IGNICIÓN SKZZ-95002
07	EXEMYS	LCACPF95003A/B/W001	PLUSPETROL	CALENTADOR DE GAS COMBUSTIBLE SKZZ-93000
08	EXEMYS	LCACPF91050W001	PLUSPETROL	ÁREA DE COMPRESORES DE AIRE Y UNIDAD DE NITRÓGENO
09	EXEMYS	LCACPF91051W002	PLUSPETROL	ÁREA DE COMPRESORES DE AIRE Y UNIDAD DE NITRÓGENO
10	STRATIX	LCACPF5E1SW601	ABB	SALA ELÉCTRICA 1
11	STRATIX	LCACPF5E1SW602	ABB	SALA ELÉCTRICA 1
12	STRATIX	LCACPF5E1SW603	ABB	SALA ELÉCTRICA 1
13	STRATIX	LCACPF5E1SW604	ABB	SALA ELÉCTRICA 1
14	STRATIX	LCACPF5E1SW605	ABB	SALA ELÉCTRICA 1
15	STRATIX	LCACPF5E1SW606	ABB	SALA ELÉCTRICA 1
16	STRATIX	LCACPF5E1SW607	ABB	SALA ELÉCTRICA 1
17	STRATIX	LCACPF5E1SW608	ABB	SALA ELÉCTRICA 1
18	STRATIX	LCACPF5E1SW609	ABB	SALA ELÉCTRICA 1
19	STRATIX	LCACPF5E1SW610	ABB	SALA ELÉCTRICA 1
20	STRATIX	LCACPF5E2SW601	ABB	SALA ELÉCTRICA 2
21	STRATIX	LCACPF5E2SW602	ABB	SALA ELÉCTRICA 2
22	STRATIX	LCACPF5E2SW603	ABB	SALA ELÉCTRICA 2
23	STRATIX	LCACPF5E2SW604	ABB	SALA ELÉCTRICA 2
24	EXEMYS	LCACPF24006SW001	PLUSPETROL	AGUA DE PRODUCCIÓN-MAZ-24006
25	STRATIX	LCACPF7BGTSW602	ABB	SALA ELÉCTRICA BT - 670-TGBT-001
26	STRATIX	LCACPF84001A/SW001	PLUSPETROL	ACEITE TÉRMICO CPF-EAP-94001A
27	EXEMYS	LCACPFCRSSW001	PLUSPETROL	SALA ELÉCTRICA 2

REFERENCIAS

021–ACAL–100–PL–K–323	CANALIZACIONES DE COMUNICACIONES GENERAL – CPF
021–ACAL–100–PL–K–324	CANALIZACIONES DE COMUNICACIONES EDIFICIO DE CONTROL – CPF
021–ACAL–100–PL–K–325	CANALIZACIONES DE COMUNICACIONES CARITA DE SEGURIDAD – CPF
021–ACAL–100–PL–K–326	CANALIZACIONES DE COMUNICACIONES SALA ELÉCTRICA 1 – CPF
021–ACAL–100–PL–K–327	CANALIZACIONES DE COMUNICACIONES SALA ELÉCTRICA 2 – CPF
021–ACAL–100–PL–K–328	CANALIZACIONES DE COMUNICACIONES SHELTER INS005 I/O REMOTAS – CPF
021–ACAL–100–PL–K–329	CANALIZACIONES DE COMUNICACIONES SHELTER INS002 I/O REMOTAS – CPF
021–ACAL–100–PL–K–330	CANALIZACIONES DE COMUNICACIONES SHELTER INS003 I/O REMOTAS – CPF
021–ACAL–100–PL–K–332	CANALIZACIONES DE COMUNICACIONES SHELTER INS004 I/O REMOTAS – CPF
021–ACAL–100–PL–K–333	CANALIZACIONES DE COMUNICACIONES ACOPIO DE MUESTRAS – CPF
021–ACAL–670–PL–K–013	CANALIZACIONES DE COMUNICACIONES EDIFICIO DE CONTROL – GENERACIÓN
021–ACAL–670–PL–K–014	CANALIZACIONES DE COMUNICACIONES SALA ELÉCTRICA – GENERACIÓN
021–ACAL–100–PL–E–320	CANALIZACIONES DE COMUNICACIONES – SCADA/PMS
021–ACAL–100–PL–LE–361	DIAGRAMA DE BLOQUES TRONCALES FO – SCADA/PMS
182–ACAL–100–PL–K–502	LAYOUT DE COMUNICACIONES
ACAL–100–PL–K–100	ARQUITECTURA DE SISTEMAS PCS
ACAL–100–PL–K–551	NETWORK ARCHITECTURE (CPF and CPF 1.5)
ACAL–00102–DC–O–0007	DIAGRAMA DE CONEXIONADO COMUNICACIONES
ACAL–00102–PL–O–0004	CANALIZACIONES DE COMUNICACIONES
ACAL–00102–PL–O–0002	ARQUITECTURA CCTV
ACAL–00102–PL–O–0003	ARQUITECTURA VOZ Y DATOS
ACAL–00102–ABBX–FMS–DC–E–0001	TOPOLOGIA DEL SISTEMA

NOMENCLATURA DE PATCH PANEL

PP–XXX–XX
- 01 AL 19 PATCH PANEL F.O. 12 PUERTOS DUPLEX MONTADO EN RACK 19"
- 20 AL 29 PATCH PANEL F.O. 06 PUERTOS DUPLEX MONTADO EN RACK 19"
- 30 AL 39 PATCH PANEL FTP 24 PUERTOS RJ–45 CAT–6 MONTADO EN RACK 19"
- XXX PATCH PANEL F.O. MONTADO EN RIEL DIN
- EQUIPO O DISPOSITIVO VER SIMBOLOGIA
- PATCH PANEL

NOMENCLATURA DE PANELES DE CONTROL

CPF–CCM–XX
- NÚMERO CONSECUTIVO
  - 01 AL 10 TABLEROS POR CERCO
  - 121 AL 60 TELECOMUNICACIONES
- SISTEMA COMUNICACIÓN
- CENTRAL PRODUCTION FACILITIES (182–26 LA CALERA (CPF 2 ó 600)

NOMENCLATURA DE EQUIPO

021–XXX–XXX–R4–XXX–XXX
- NÚMERO CONSECUTIVO
- EQUIPO O DISPOSITIVO VER SIMBOLOGIA
- SISTEMA
  - 01 – CABLEADO ESTRUCTURADO
  - 02 – CCTV CIRCUITO CERRADO DE TV.
  - 03 – CONTROL DE ACCESOS
  - 04 – VOIP VOZ Y DATOS
  - 05 – WIFI
- SUB AREA
  - BGP – BALANCE DE PLANTA
  - R2 – SHELTER INS002
  - R3 – SHELTER INS003
  - R4 – SHELTER INS004
  - R5 – SHELTER INS005
  - R6 – SHELTER INS006
  - R7 – SHELTER INS007
  - SE1 – SALA ELECTRICA 1
  - SE2 – SALA ELECTRICA 2
  - SE3 – SALA ELECTRICA 3
  - SE4 – SALA ELECTRICA 4
  - SE5 – SALA ELECTRICA GENERACIÓN
  - SCCPF – SALA CONTROL CPF
  - LAB – ACOPIO DE MUESTRAS
  - VIG – VIGILANCIA
  - 191 – SKID DE COMPRESOR 19151
  - 192 – SKID DE COMPRESOR 19250
  - 193 – SKID DE COMPRESOR 19350
  - 194 – SKID DE COMPRESOR BOOSTER #1
  - 195 – SKID DE COMPRESOR BOOSTER #2
  - 196 – SKID DE COMPRESOR BOOSTER #3
  - 240 – SKID DE AGUA DE PRODUCCIÓN
  - 670004A – SKID COMPRESOR DE AIRE SKZZ-67002
  - 670006B – SKID COMPRESOR DE AIRE SKZZ-67002
  - 670014 – SKID GAS COMBUSTIBLE SKZZ-67001
  - 670018 – SKID GAS COMBUSTIBLE SKZZ-67001
  - 910 – SKID DE COMPRESORES DE AIRE
  - 920 – SKID DE MEMBRANAS
  - 930 – SKID DE CALENTADOR DE GAS
  - 940 – SKID DE HORNO HOT OIL
  - 950 – SKID DE CALENTADOR KOD
  - 960 – SKID ACEITE TÉRMICO
  - 99004 – SEDIMENTACIÓN/FILTRADO FINO DE AGUA CRUDA
  - 99002 – FILTRADO GRUESO DE AGUA CRUDA
  - TB – TORRE BARDA
  - CCM001A – CENTRO DE CONTROL DE MOTORES 001 SEMIBARRA "A"
  - CCM001B – CENTRO DE CONTROL DE MOTORES 001 SEMIBARRA "B"
  - CCM002A – CENTRO DE CONTROL DE MOTORES 002 SEMIBARRA "A"
  - CCM002B – CENTRO DE CONTROL DE MOTORES 002 SEMIBARRA "B"
  - CCM003A – CENTRO DE CONTROL DE MOTORES 003 SEMIBARRA "A"
  - CCM003B – CENTRO DE CONTROL DE MOTORES 003 SEMIBARRA "B"
  - CCM003C – CENTRO DE CONTROL DE MOTORES 003 SEMIBARRA "C"
  - TGBT – TABLERO GENERAL BAJA TENSIÓN
  - FUR – FLARE
  - CCM – CENTRO DE CONTROL DE MOTORES EPF
  - CCM01 – GABINETE DE CONTROL 01
- AREA
  - 100 – CPF
  - 670 – GENERACIÓN
  - 021 – CENTRAL PRODUCTION FACILITES (CNO–26 LA CALERA
  - 182 – CNO–26 LA CALERA
  - 182 – AMPLIACIÓN CPF
  - 330 – CENTRAL PRODUCTION FACILITES 2

NOMENCLATURA DE CABLE

021–XXX–XXX–XX–XXX–XXX–XXX
- CAPACIDAD EN:
  - #F – PARES
  - #C – CONDUCTORES
  - #CO – CONDUCTORES ÓPTICOS
- NÚMERO DE SEGMENTO POR SISTEMA + CONSECUTIVO
  - 1XX – CABLEADO ESTRUCTURADO
  - 2XX – CCTV CIRCUITO CERRADO DE TV.
  - 3XX – CONTROL DE ACCESOS
  - 4XX – VOIP VOZ Y DATOS
  - 5XX – WIFI
- TIPO DE CABLE
  - F.O.
  - FTP
  - MC
- SISTEMA
  - 01 – CABLEADO ESTRUCTURADO
  - 02 – CCTV CIRCUITO CERRADO DE TV.
  - 03 – CONTROL DE ACCESOS
  - 04 – VOIP VOZ Y DATOS
  - 05 – WIFI
- SUB AREA
  - BGP – BALANCE DE PLANTA
  - R2 – SHELTER INS002
  - R3 – SHELTER INS003
  - R4 – SHELTER INS004
  - R5 – SHELTER INS005
  - R6 – SHELTER INS006
  - R7 – SHELTER INS007
  - SE1 – SALA ELECTRICA 1
  - SE2 – SALA ELECTRICA 2
  - SE3 – SALA ELECTRICA 3
  - SE4 – SALA ELECTRICA 4
  - SE5 – SALA ELECTRICA GENERACIÓN
  - SCCPF – SALA CONTROL CPF
  - LAB – ACOPIO DE MUESTRAS
  - VIG – VIGILANCIA
  - 191 – SKID DE COMPRESOR 19151
  - 192 – SKID DE COMPRESOR 19250
  - 193 – SKID DE COMPRESOR 19350
  - 194 – SKID DE COMPRESOR BOOSTER #1
  - 195 – SKID DE COMPRESOR BOOSTER #2
  - 196 – SKID DE COMPRESOR BOOSTER #3
  - 240 – SKID DE AGUA DE PRODUCCIÓN
  - 670004A – SKID COMPRESOR DE AIRE SKZZ-67002
  - 670006B – SKID COMPRESOR DE AIRE SKZZ-67002
  - 670014 – SKID GAS COMBUSTIBLE SKZZ-67001
  - 670018 – SKID GAS COMBUSTIBLE SKZZ-67001
  - 910 – SKID DE COMPRESORES DE AIRE
  - 920 – SKID DE MEMBRANAS
  - 930 – SKID DE CALENTADOR DE GAS
  - 940 – SKID DE HORNO HOT OIL
  - 950 – SKID DE CALENTADOR KOD
  - 960 – SKID ACEITE TÉRMICO
  - 99004 – SEDIMENTACIÓN/FILTRADO FINO DE AGUA CRUDA
  - 99002 – FILTRADO GRUESO DE AGUA CRUDA
  - TB – TORRE BARDA
  - CCM001A – CENTRO DE CONTROL DE MOTORES 001 SEMIBARRA "A"
  - CCM001B – CENTRO DE CONTROL DE MOTORES 001 SEMIBARRA "B"
  - CCM002A – CENTRO DE CONTROL DE MOTORES 002 SEMIBARRA "A"
  - CCM002B – CENTRO DE CONTROL DE MOTORES 002 SEMIBARRA "B"
  - CCM003A – CENTRO DE CONTROL DE MOTORES 003 SEMIBARRA "A"
  - CCM003B – CENTRO DE CONTROL DE MOTORES 003 SEMIBARRA "B"
  - CCM003C – CENTRO DE CONTROL DE MOTORES 003 SEMIBARRA "C"
  - TGBT – TABLERO GENERAL BAJA TENSIÓN
  - FUR – FLARE
  - CCM – CENTRO DE CONTROL DE MOTORES EPF
  - CCM01 – GABINETE DE CONTROL 01
- AREA
  - 100 – CPF
  - 670 – GENERACIÓN
  - 021 – CENTRAL PRODUCTION FACILITES (CNO–26 LA CALERA
  - 182 – AMPLIACIÓN CPF
  - 330 – CPF2

SISTEMA DE CONTROL DE ACCESO Y SEGURIDAD (SCA)

SÍMBOLO	EQUIPO	NOMBRE
	CRI	CAJA DE CONEXIONADO, A PRUEBA DE AGUA, PARA INTERIOR
	PP-FO-24	PATCH PANEL, PARA FIBRA ÓPTICA, 12 PUERTOS DUPLEX
	PP-FO-12	PATCH PANEL, PARA FIBRA ÓPTICA, 6 PUERTOS DUPLEX
	SW	SWITCH ETHERNET / FIBRA ÓPTICA MONOMODO, MONTAJE EN RIEL DIN
	RJ-45	CONECTOR RJ-45
	ODF	DISTRIBUIDOR DE FIBRA ÓPTICA
		DIVISIÓN ÁREAS
		DIVISIÓN ZONAS
		EQUIPOS
		FIBRA ÓPTICA MONOMODO 6H
		FIBRA ÓPTICA MONOMODO 24H
		CABLE FTP CATEGORÍA 6
		CABLE RS-485

REV.	DESCRIPCION	FECHA	POR	CHK.	APPD.
0	PARA CONSTRUCCIÓN	05/08/2026	IPS	EGN	AZA
A	PARA APROBACIÓN	15/05/2026	IPS	EGN	AZA

AESA Nº: 5155-00-0000-IG-IN-DF-001

pluspetrol
FACILITIES ENG. & PROJECTS

PROYECTO: LA CALERA CPF2 - FASE 2
FASE: INGENIERÍA DE DETALLE
TITULO:

DIAGRAMA EN BLOQUES COMUNICACIONES

Toda la información contenida en la presente documentación es confidencial y de propiedad de Pluspetrol Facilities Eng. & Projects. Prohibida su copia, total o parcial, sin autorización previa.

ESCALA: S/E

N° DOCUMENTO: ACAL-00102-PL-O-0001

REVISIÓN: 0

REMPLAZA: 226-ACAL-100-PL-K-305

Pág.: 1 de 2

TABLA 2

ITEM	SWITCH	TAG-SWITCH	SUMINISTRADO	UBICACIÓN
01	STRATIX	LCACPF2R7RB500	AESA (INAUCO)	SHELTER INS007
02	STRATIX	LCACPF2SE3SW001	AESA (INAUCO)	SALA ELÉCTRICA 3
03	STRATIX	LCACPF2SE3SW002	AESA (INAUCO)	SALA ELÉCTRICA 3
04	STRATIX	LCACPF2SE4SW001	AESA (INAUCO)	SALA ELÉCTRICA 4
05	STRATIX	LCACPF2SE4SW002	AESA (INAUCO)	SALA ELÉCTRICA 4
06	STRATIX	LCACPF2931105W001	AESA (INAUCO)	SKID DE GAS COMBUSTIBLE SKZZ-93110
07	STRATIX	LCACPF2942201SW001	AESA (INAUCO)	HORNO DE HOT OIL EAP-94201A
08	STRATIX	LCACPF2951305W001	AESA (INAUCO)	CALENTADOR DE KOD EAP-95130A/B
09	STRATIX	LCACPF2910SW003	AESA (INAUCO)	ÁREA DE COMPRESORES DE AIRE Y UNIDAD DE NITRÓGENO
10	STRATIX	LCACPF2910SW004	AESA (INAUCO)	ÁREA DE COMPRESORES DE AIRE Y UNIDAD DE NITRÓGENO
11	STRATIX	LCACPF2904SW001	AESA (INAUCO)	CALENTADOR DE ACEITE LUBRICANTE EAP-90420/90450
12				
13				
14				
15				
16				
17				
18				
19				
20				
21				
22				
23				
24				

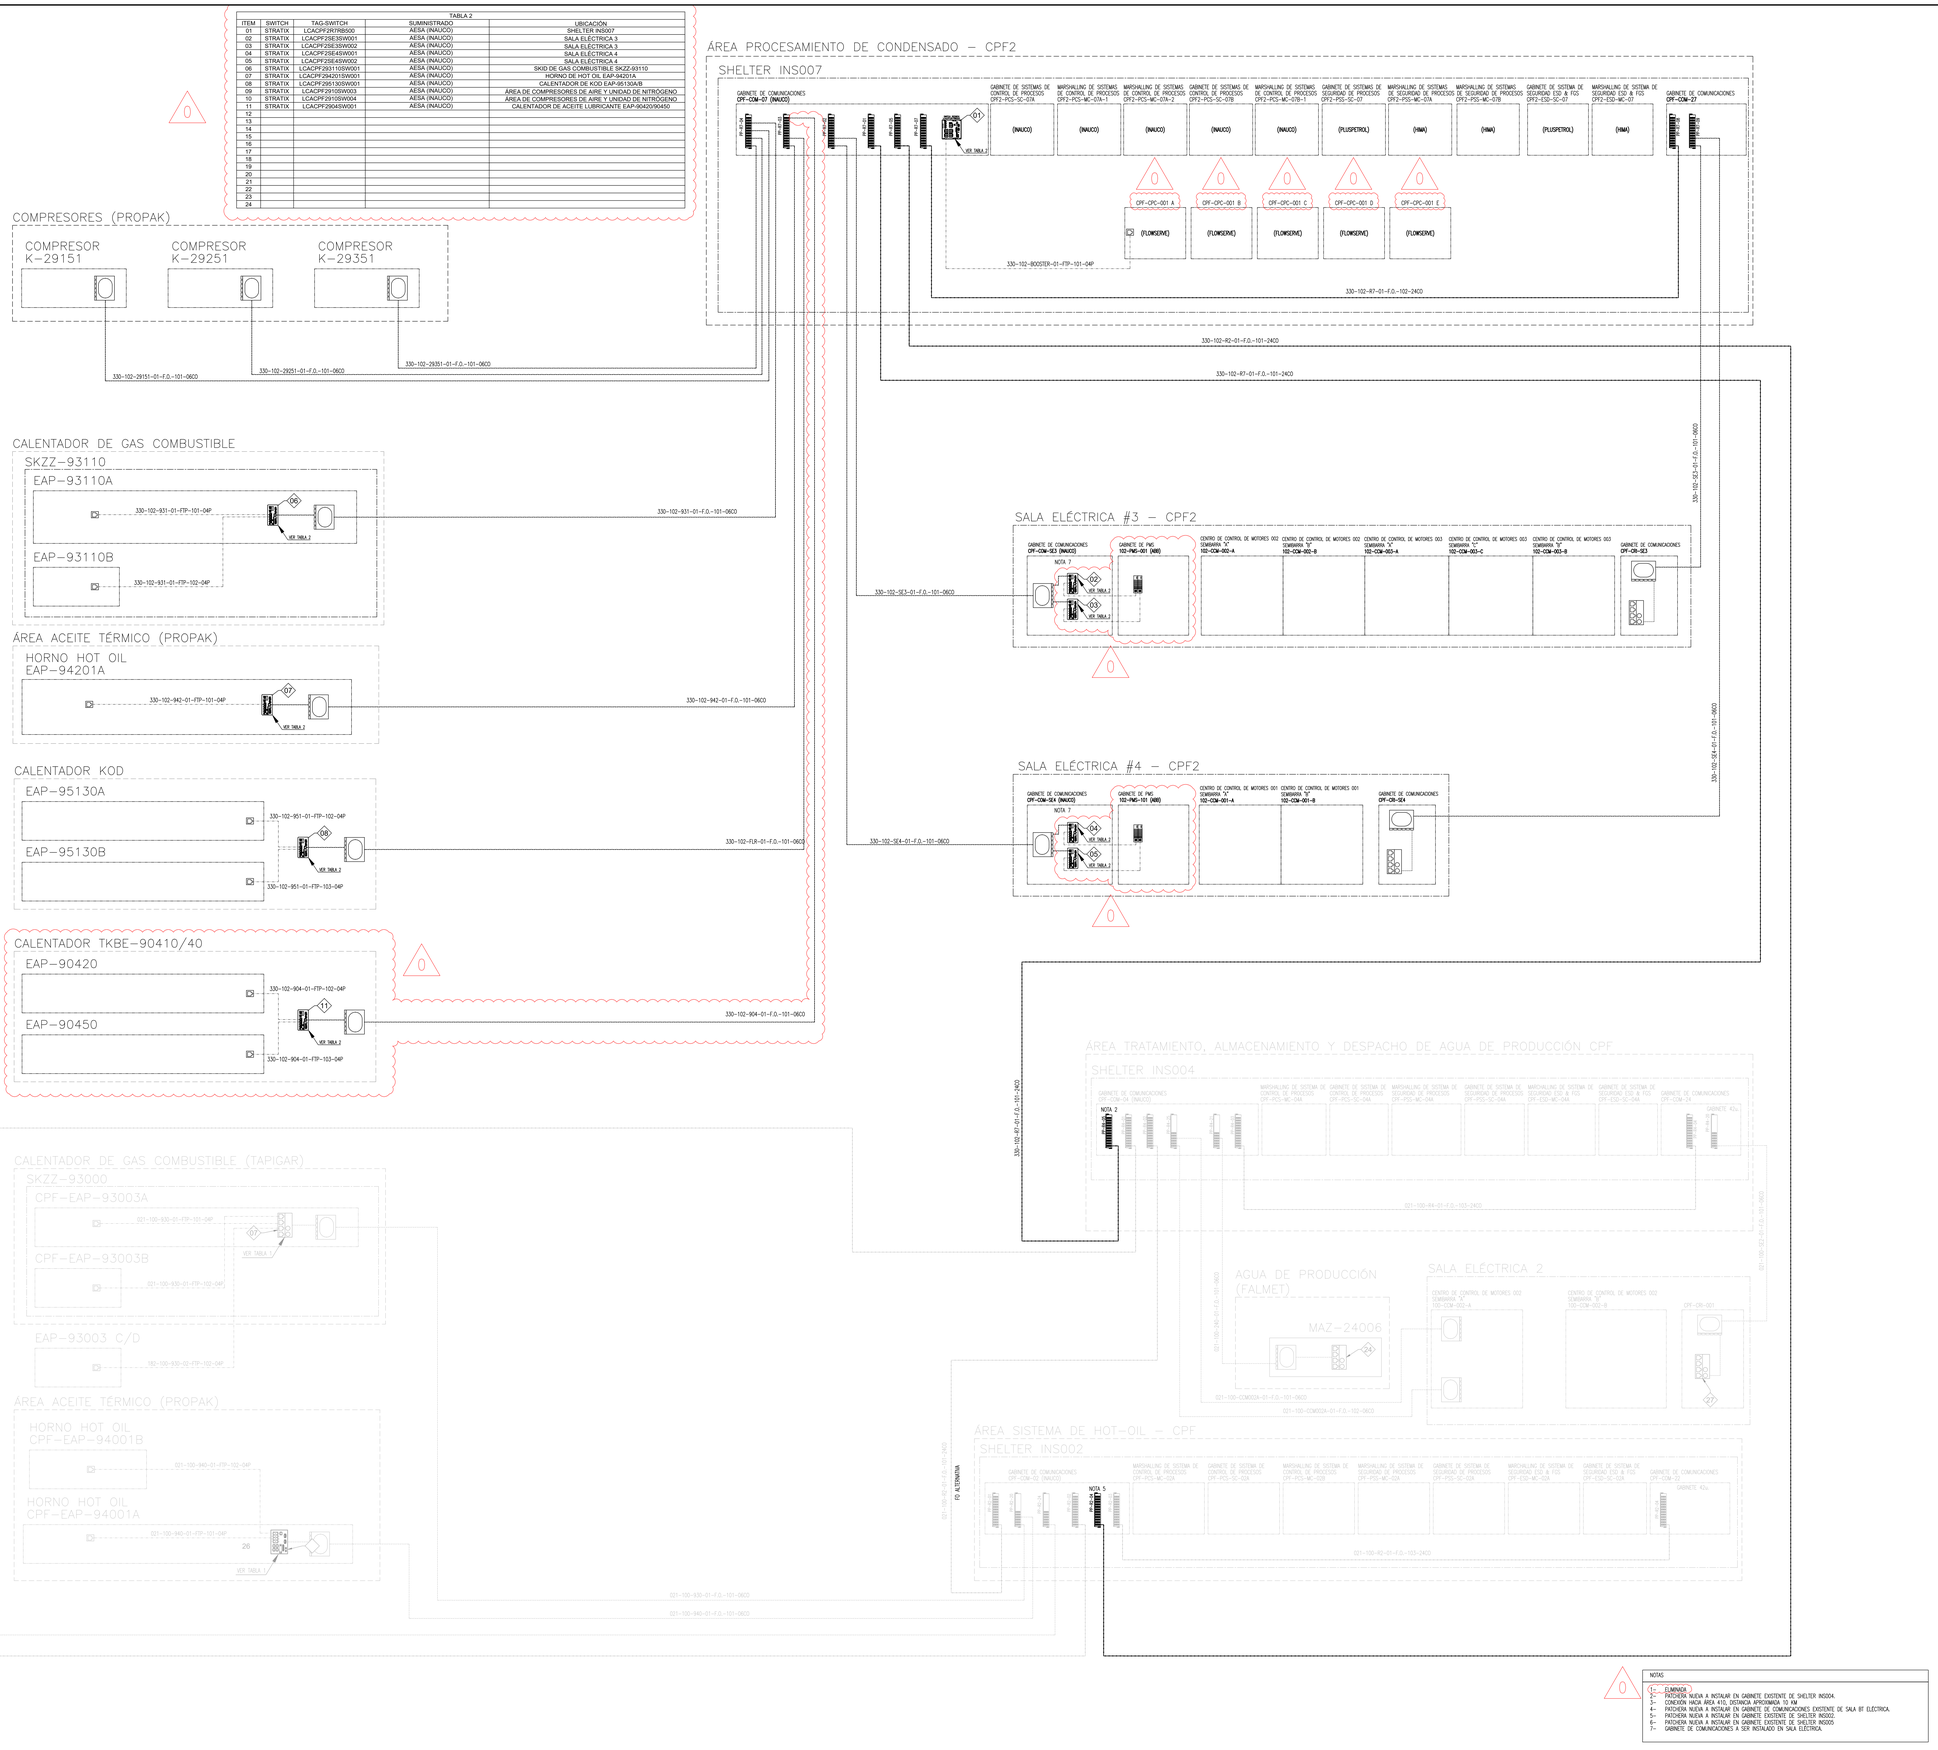

NOTAS:

1.- ELIMINADA.
2.- PATCHERA NUEVA A INSTALAR EN GABINETE EXISTENTE DE SHELTER INS004.
3.- CONEXIÓN HACIA ÁREA 4112, DISTANCIA APROXIMADA 15 KM.
4.- PATCHERA NUEVA A INSTALAR EN GABINETE DE COMUNICACIONES EXISTENTE DE SALA BT ELÉCTRICA.
5.- PATCHERA NUEVA A INSTALAR EN GABINETE EXISTENTE DE SHELTER INS003.
6.- PATCHERA NUEVA A INSTALAR EN GABINETE EXISTENTE DE SHELTER INS003.
7.- GABINETE DE COMUNICACIONES A SER INSTALADO EN SALA ELÉCTRICA.

REFERENCIAS

021-ACAL-100-PL-K-323	CANALIZACIONES DE COMUNICACIONES GENERAL – CPF
021-ACAL-100-PL-K-324	CANALIZACIONES DE COMUNICACIONES EDIFICIO DE CONTROL – CPF
021-ACAL-100-PL-K-325	CANALIZACIONES DE COMUNICACIONES CARITA DE SEGURIDAD – CPF
021-ACAL-100-PL-K-326	CANALIZACIONES DE COMUNICACIONES SALA ELÉCTRICA 1 – CPF
021-ACAL-100-PL-K-327	CANALIZACIONES DE COMUNICACIONES SALA ELÉCTRICA 2 – CPF
021-ACAL-100-PL-K-328	CANALIZACIONES DE COMUNICACIONES SHELTER INS005 I/O REMOTAS – CPF
021-ACAL-100-PL-K-329	CANALIZACIONES DE COMUNICACIONES SHELTER INS002 I/O REMOTAS – CPF
021-ACAL-100-PL-K-330	CANALIZACIONES DE COMUNICACIONES SHELTER INS003 I/O REMOTAS – CPF
021-ACAL-100-PL-K-332	CANALIZACIONES DE COMUNICACIONES SHELTER INS004 I/O REMOTAS – CPF
021-ACAL-100-PL-K-333	CANALIZACIONES DE COMUNICACIONES ACOPIO DE MUESTRAS – CPF
021-ACAL-670-PL-K-013	CANALIZACIONES DE COMUNICACIONES EDIFICIO DE CONTROL – GENERACIÓN
021-ACAL-670-PL-K-014	CANALIZACIONES DE COMUNICACIONES SALA ELÉCTRICA – GENERACIÓN
021-ACAL-100-PL-K-320	CANALIZACIONES DE COMUNICACIONES – SCADA/PMC
021-ACAL-100-PL-K-361	DIAGRAMA DE BLOQUES TRONCALES FO – SCADA/PMS
182-ACAL-100-PL-K-502	LAYOUT DE COMUNICACIONES
ACAL-100-PL-K-100	ARQUITECTURA DE SISTEMAS PCS
ACAL-100-PL-K-551	NETWORK ARCHITECTURE (CPF and CPF 1.5)
ACAL-00102-DC-O-0007	DIAGRAMA DE CONEXIONADO COMUNICACIONES
ACAL-00102-PL-O-0004	CANALIZACIONES DE COMUNICACIONES
ACAL-00102-PL-O-0002	ARQUITECTURA CCTV
ACAL-00102-PL-O-0003	ARQUITECTURA VOZ Y DATOS
ACAL-00102-ABBX-PMS-DC-E-0001	TOPOLOGÍA DEL SISTEMA

NOMENCLATURA DE PATCH PANEL

PP-XXX-XX
- 01 AL 19 PATCH PANEL F.O. 12 PUERTOS DUPLEX MONTADO EN RACK 19"
- 20 AL 29 PATCH PANEL F.O. 06 PUERTOS DUPLEX MONTADO EN RACK 19"
- 30 AL 39 PATCH PANEL FTP 24 PUERTOS RJ-45 CAT-6 MONTADO EN RACK 19"
- XXX PATCH PANEL F.O. MONTADO EN RIEL DIN
- EQUIPO O DISPOSITIVO VER SIMBOLOGÍA
- PATCH PANEL

NOMENCLATURA DE PANELES DE CONTROL

CPF-CCM-XX
- NÚMERO CONSECUTIVO
- 01 AL 10 TABLEROS POR CIRCIS.
- 21 AL 60 TELECOMUNICACIONES
- SISTEMA COMUNICACIÓN
- CENTRAL PRODUCTION FACILITIES (182–26 LA CALERA (CPF 2 ÁREA))

NOMENCLATURA DE EQUIPO

021-XXX-XXX-XX-XXX-XXX
- NÚMERO CONSECUTIVO
- EQUIPO O DISPOSITIVO VER SIMBOLOGÍA
- SISTEMA
  - 01 – CABLEADO ESTRUCTURADO
  - 02 – CCTV CIRCUITO CERRADO DE TV.
  - 03 – CONTROL DE ACCESOS
  - 04 – VOIP VOZ Y DATOS
  - 05 – WIFI
- SUB ÁREA
  - BOP – BALANCE DE PLANTA
  - R2 – SHELTER INS002
  - R3 – SHELTER INS003
  - R4 – SHELTER INS004
  - R5 – SHELTER INS005
  - SE1 – SALA ELÉCTRICA 1
  - SE2 – SALA ELÉCTRICA 2
  - SCG – SALA CONTROL GENERACIÓN
  - SEG – SALA ELECTRICA GENERACIÓN
  - SCCPF – SALA CONTROL CPF
  - LAB – ACOPIO DE MUESTRAS
  - VIG – VIGILANCIA
  - 191 – SKID DE COMPRESOR 19151
  - 192 – SKID DE COMPRESOR 19250
  - 193 – SKID DE COMPRESOR 19350
  - 240 – SKID DE AGUA DE PRODUCCIÓN
  - 670064 – SKID COMPRESOR DE AIRE SKZZ-67002
  - 670069 – SKID COMPRESOR DE AIRE SKZZ-67002
  - 670014 – SKID GAS COMBUSTIBLE SKZZ-67001
  - 670016 – SKID GAS COMBUSTIBLE SKZZ-67001
  - 910 – SKID DE COMPRESORES DE AIRE
  - 920 – SKID DE MEMBRANAS
  - 930 – SKID DE CALENTADOR DE GAS
  - 940 – SKID DE HORNO HOT OIL
  - 950 – SKID DE CALENTADOR KOD
  - 960 – SKID DE BOMBA DE IKO
  - 99004 – SEDIMENTACIÓN/FILTRADO FINO DE AGUA CRUDA
  - 99002 – FILTRADO GRUESO DE AGUA CRUDA
  - TB – TORRE BAISA
  - CCM001A – CENTRO DE CONTROL DE MOTORES 001 SEMIBARRA "A"
  - CCM001B – CENTRO DE CONTROL DE MOTORES 001 SEMIBARRA "B"
  - CCM002A – CENTRO DE CONTROL DE MOTORES 002 SEMIBARRA "A"
  - CCM002B – CENTRO DE CONTROL DE MOTORES 002 SEMIBARRA "B"
  - CCM003A – CENTRO DE CONTROL DE MOTORES 003 SEMIBARRA "A"
  - CCM003B – CENTRO DE CONTROL DE MOTORES 003 SEMIBARRA "B"
  - CCM003C – CENTRO DE CONTROL DE MOTORES 003 SEMIBARRA "C"
  - TGBT – TABLERO GENERAL BAJA TENSIÓN
  - FLR – FLARE
  - CCM – CENTRO DE CONTROL DE MOTORES EPF
  - GC01 – GABINETE DE CONTROL 01
- ÁREA
  - 100 – CPF
  - 670 – GENERACIÓN
  - R3 – SHELTER INS003
  - SE3 – SALA ELÉCTRICA 3
  - SE4 – SALA ELÉCTRICA 4
  - 194 – SKID DE COMPRESOR BOOSTER #1
  - 195 – SKID DE COMPRESOR BOOSTER #2
  - 196 – SKID DE COMPRESOR BOOSTER #3
  - 291 – COMPRESOR DE GAS MULTISERVICIO #1
  - 292 – COMPRESOR DE GAS MULTISERVICIO #2
  - 293 – COMPRESOR DE GAS MULTISERVICIO #3
  - 931 – SKID DE GAS COMBUSTIBLE SKZZ-93110
  - 942 – SKID DE HORNO HOT OIL
  - 67040 – SKID DE GAS COMBUSTIBLE SKZZ-67040
- 182 – AMPLIACIÓN CPF
- 330 – CENTRAL PRODUCTION FACILITIES 2

NOMENCLATURA DE CABLE

021-XXX-XXX-XX-XXX-XXX
- CAPACIDAD EN:
  - MT – PARES
  - CO – CONDUCTORES
  - FO – CONDUCTORES ÓPTICOS
- NÚMERO DE SEGMENTO POR SISTEMA + CONSECUTIVO
- TXX – CABLEADO ESTRUCTURADO
- 2XX – CCTV CIRCUITO CERRADO DE TV.
- 3XX – CONTROL DE ACCESOS
- 4XX – VOIP VOZ Y DATOS
- 5XX – WIFI
- TIPO DE CABLE
  - F.O.
  - FTP
  - MC
- SISTEMA
  - 01 – CABLEADO ESTRUCTURADO
  - 02 – CCTV CIRCUITO CERRADO DE TV.
  - 03 – CONTROL DE ACCESOS
  - 04 – VOIP VOZ Y DATOS
  - 05 – WIFI
- SUB ÁREA
  - BOP – BALANCE DE PLANTA
  - R2 – SHELTER INS002
  - R3 – SHELTER INS003
  - R4 – SHELTER INS004
  - R5 – SHELTER INS005
  - SE1 – SALA ELÉCTRICA 1
  - SE2 – SALA ELÉCTRICA 2
  - SCG – SALA CONTROL GENERACIÓN
  - SEG – SALA ELECTRICA GENERACIÓN
  - SCCPF – SALA CONTROL CPF
  - LAB – ACOPIO DE MUESTRAS
  - VIG – VIGILANCIA
  - 191 – SKID DE COMPRESOR 19151
  - 192 – SKID DE COMPRESOR 19250
  - 193 – SKID DE COMPRESOR 19350
  - 240 – SKID DE AGUA DE PRODUCCIÓN
  - 670064 – SKID COMPRESOR DE AIRE SKZZ-67002
  - 670069 – SKID COMPRESOR DE AIRE SKZZ-67002
  - 670014 – SKID GAS COMBUSTIBLE SKZZ-67001
  - 670016 – SKID GAS COMBUSTIBLE SKZZ-67001
  - 910 – SKID DE COMPRESORES DE AIRE
  - 920 – SKID DE MEMBRANAS
  - 930 – SKID DE CALENTADOR DE GAS
  - 940 – SKID DE HORNO HOT OIL
  - 950 – SKID DE CALENTADOR KOD
  - 960 – SKID DE BOMBA DE IKO
  - 99004 – SEDIMENTACIÓN/FILTRADO FINO DE AGUA CRUDA
  - 99002 – FILTRADO GRUESO DE AGUA CRUDA
  - TB – TORRE BAISA
  - CCM001A – CENTRO DE CONTROL DE MOTORES 001 SEMIBARRA "A"
  - CCM001B – CENTRO DE CONTROL DE MOTORES 001 SEMIBARRA "B"
  - CCM002A – CENTRO DE CONTROL DE MOTORES 002 SEMIBARRA "A"
  - CCM002B – CENTRO DE CONTROL DE MOTORES 002 SEMIBARRA "B"
  - CCM003A – CENTRO DE CONTROL DE MOTORES 003 SEMIBARRA "A"
  - CCM003B – CENTRO DE CONTROL DE MOTORES 003 SEMIBARRA "B"
  - CCM003C – CENTRO DE CONTROL DE MOTORES 003 SEMIBARRA "C"
  - TGBT – TABLERO GENERAL BAJA TENSIÓN
  - FLR – FLARE
  - CCM – CENTRO DE CONTROL DE MOTORES EPF
  - GC01 – GABINETE DE CONTROL 01
- ÁREA
  - 100 – CPF
  - 670 – GENERACIÓN
  - R3 – SHELTER INS003
  - SE3 – SALA ELÉCTRICA 3
  - SE4 – SALA ELÉCTRICA 4
  - 194 – SKID DE COMPRESOR BOOSTER #1
  - 195 – SKID DE COMPRESOR BOOSTER #2
  - 196 – SKID DE COMPRESOR BOOSTER #3
  - 291 – COMPRESOR DE GAS MULTISERVICIO #1
  - 292 – COMPRESOR DE GAS MULTISERVICIO #2
  - 293 – COMPRESOR DE GAS MULTISERVICIO #3
  - 931 – SKID DE GAS COMBUSTIBLE SKZZ-93110
  - 942 – SKID DE HORNO HOT OIL
  - 67040 – SKID DE GAS COMBUSTIBLE SKZZ-67040
- 021 – CENTRAL PRODUCTION FACILITES – CNO-26 LA CALERA 182 – AMPLIACIÓN CPF 330 – CPF2

SISTEMA DE CONTROL DE ACCESO Y SEGURIDAD (SCA)

SÍMBOLO	EQUIPO	NOMBRE
	CRI	CAJA DE CONEXIONADO, A PRUEBA DE AGUA, PARA INTERIOR
	PP-FO-24	PATCH PANEL, PARA FIBRA ÓPTICA, 12 PUERTOS DUPLEX
	PP-FO-12	PATCH PANEL, PARA FIBRA ÓPTICA, 6 PUERTOS DUPLEX
	SW	SWITCH ETHERNET / FIBRA ÓPTICA MONOMODO, MONTAJE EN RIEL DIN
	RJ-45	CONECTOR RJ-45
	ODF	DISTRIBUIDOR DE FIBRA ÓPTICA
		DIVISIÓN ÁREAS
		DIVISIÓN ZONAS
		EQUIPOS
		FIBRA ÓPTICA MONOMODO 8H
		FIBRA ÓPTICA MONOMODO 24H
		CABLE FTP CATEGORÍA 6
		CABLE RS-485

REV.	DESCRIPCION	FECHA	POR	CHK.	APPD.
0	PARA CONSTRUCCIÓN	05/08/2026	IPS	EGN	AZA
A	PARA APROBACIÓN	15/05/2026	IPS	EGN	AZA

AESA

AESA Nº: 5155-00-0000-IG-IN-DF-001

pluspetrol

FACILITIES ENG. & PROJECTS

PROYECTO: LA CALERA CPF2 - FASE 2

FASE: INGENIERÍA DE DETALLE

TÍTULO:

DIAGRAMA EN BLOQUES COMUNICACIONES

Toda la información contenida en la presente es de carácter confidencial y de propiedad de Pluspetrol, siendo prohibida su reproducción o copia, total o parcial, sin autorización previa.

ESCALA:

Nº DOCUMENTO: ACAL-00102-PL-O-0001

REVISIÓN: 0

REMPLAZA: 226-ACAL-100-PL-K-305