


PLANTA

EQUIPOS NO PROVISTOS POR ABB

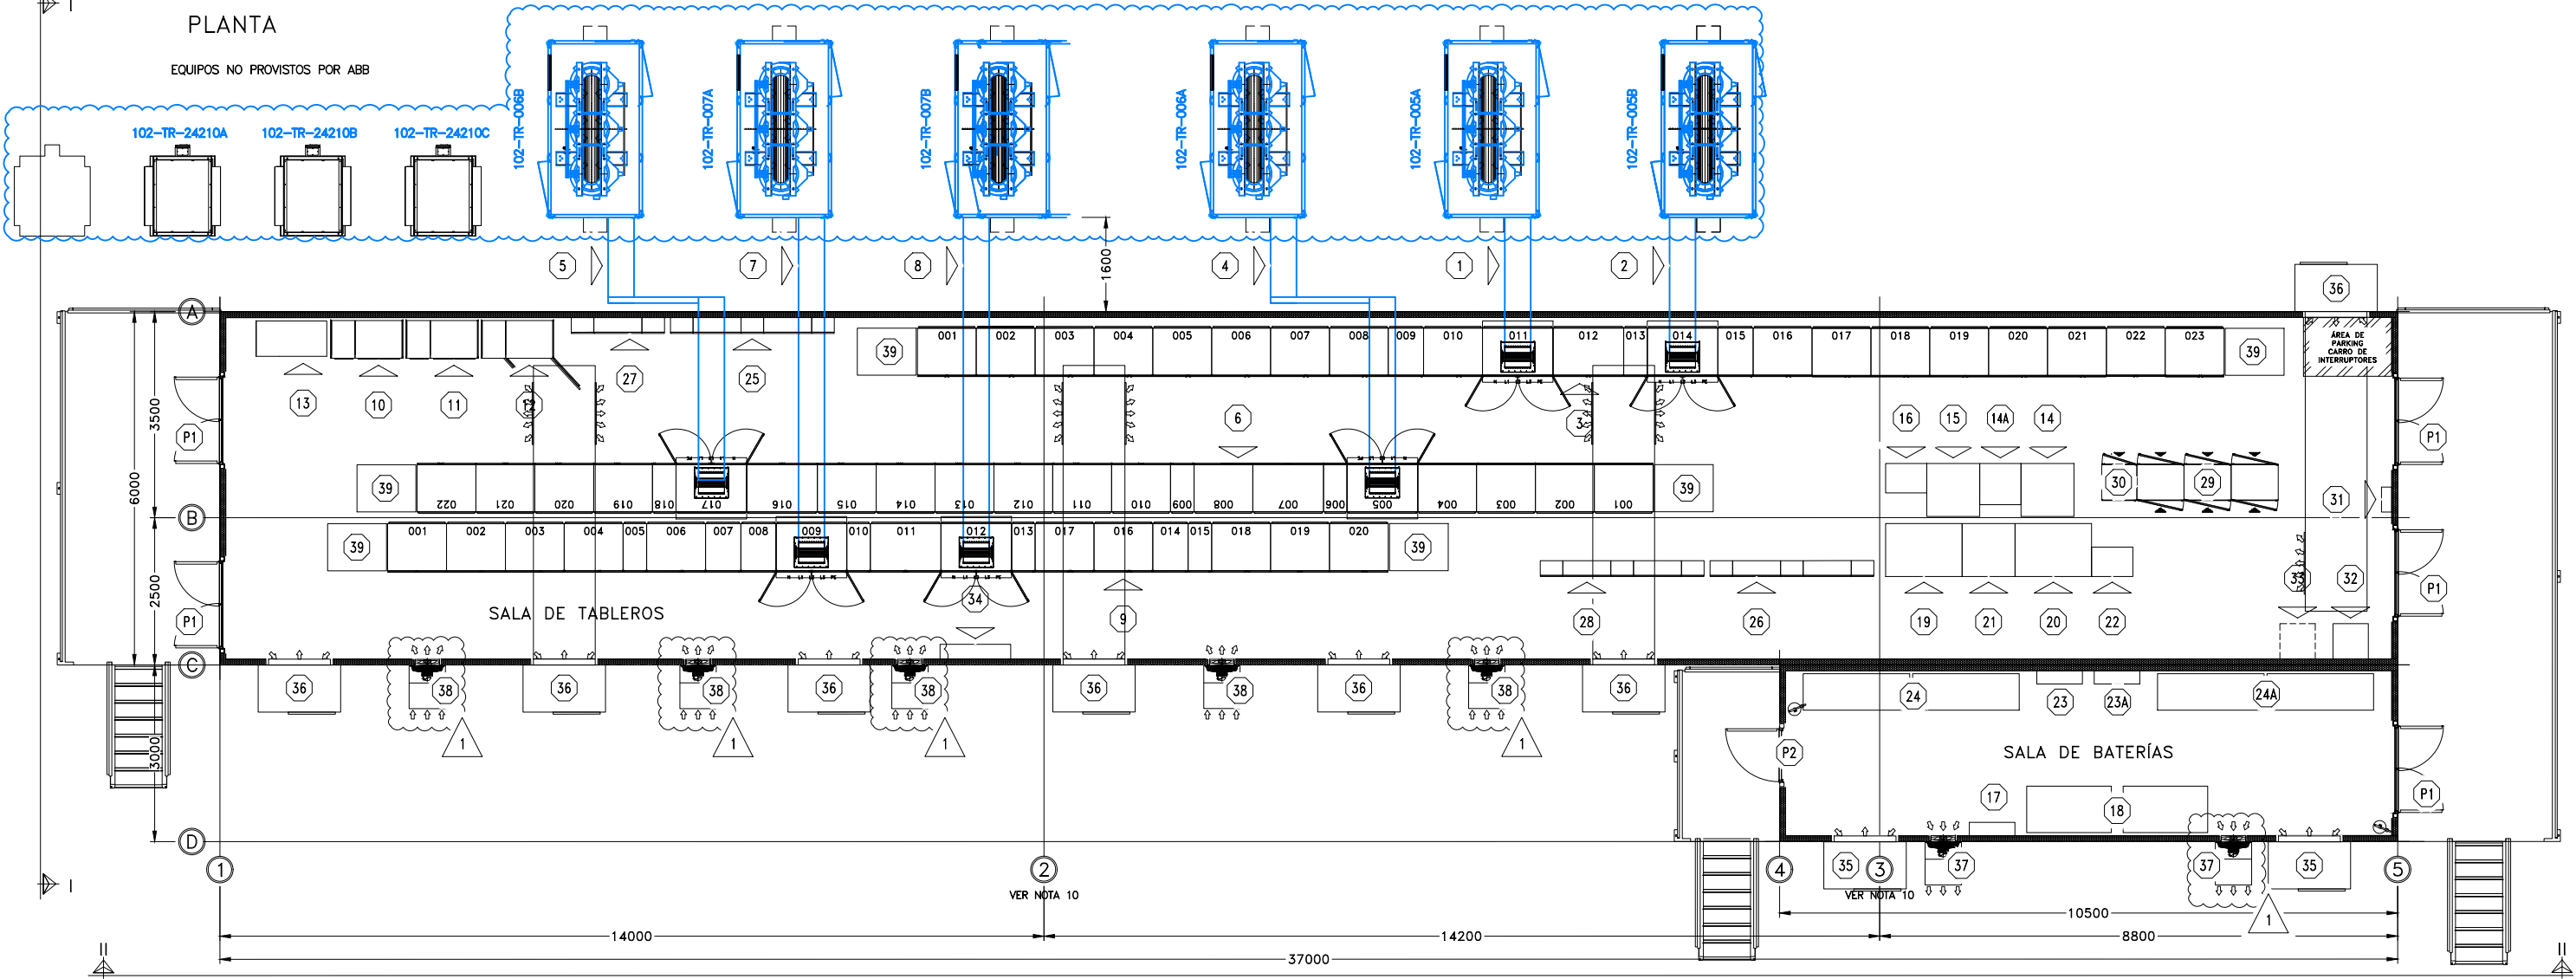

LISTA DE EQUIPOS A PROVEER ABB

REF.	TAG	DESCRIPCIÓN	PESO [kg]	DISIPACIÓ [W]
---	SE #3	Sala Eléctrica Modular, dimensiones estimadas en mts, L= 37,0 x A= 6,0 x H _{MEDIOGR} = 3,7. Se excluye en esta medida la Sala de Baterías.	---	---
P1	---	Portón de Acceso de Equipos/Personal, ancho libre 1400mm (2 hojas, 900mm + 500mm) x alto libre 2100mm + paño removible de 600mm quedando una altura libre total de 2700mm.	---	---
P2	---	Puerta de Acceso de Personal, ancho libre 900mm x alto libre 2100mm.	---	---
1	102-DB-005A	Ducto de Barras, 3F + N, barras de Cu, un tramo para instalación en intemperie, un tramo para instalación interior - 4000A - 95/120 kA (1s) - 380 / 220 Vca	---	700
2	102-DB-005B	Ducto de Barras, 3F + N, barras de Cu, un tramo para instalación en intemperie, un tramo para instalación interior - 4000A - 95/120 kA (1s) - 380 / 220 Vca	---	700
3	102-CCM-005	Centro de Control de Motores, ejecución extralibre, a prueba de arco interno, doble barra ("A" y "B") con acople, conforme IEC 61439-1/2 - 4000A - 65kA (1s) - 380/220 Vca	8900	10226
4	102-DB-006A	Ducto de Barras, 3F + N, barras de Cu, un tramo para instalación en intemperie, un tramo para instalación interior - 4000A - 95/120 kA (1s) - 380 / 220 Vca	---	2800
5	102-DB-006B	Ducto de Barras, 3F + N, barras de Cu, un tramo para instalación en intemperie, un tramo para instalación interior - 4000A - 95/120 kA (1s) - 380 / 220 Vca	---	2800
6	102-CCM-006	Centro de Control de Motores, ejecución extralibre, a prueba de arco interno, doble barra ("A" y "B") con acople, conforme IEC 61439-1/2 - 4000A - 65kA (1s) - 380/220 Vca	8800	7862
7	102-DB-007A	Ducto de Barras, 3F + N, barras de Cu, un tramo para instalación en intemperie, un tramo para instalación interior - 4000A - 95/120 kA (1s) - 380 / 220 Vca	---	4200
8	102-DB-007B	Ducto de Barras, 3F + N, barras de Cu, un tramo para instalación en intemperie, un tramo para instalación interior - 4000A - 95/120 kA (1s) - 380 / 220 Vca	---	4200
9	102-CCM-007	Centro de Control de Motores, ejecución extralibre, a prueba de arco interno, doble barra ("A" y "B") con acople, conforme IEC 61439-1/2 - 4000A - 65kA (1s) - 380/220 Vca	7900	7780
10	102-DP-VFD-24210A	Tablero metálico autoportante, instalación interior, IP 22, ejecución fija. Acceso de cables inferior. Compuesto por: Interruptor Caja moldeada, Variador de frecuencia p/motor de bomba de condensado PAZ-24210A. Lógica de comando 220/24Vca. Luces indicadoras y selectora en puerta. - 373kW - 380 Vca - 3F	1180	15000

11	102-DP-VFD-24210B	Tablero metálico autoportante, instalación interior, IP 22, ejecución fija. Acceso de cables inferior. Compuesto por: Interruptor Caja moldeada, Variador de frecuencia p/motor de bomba de condensado PAZ-24210B. Lógica de comando 220/24Vca. Luces indicadoras y selectora en puerta. - 373kW - 380 Vca - 3F	1180	15000
12	102-DP-VFD-24210C	Tablero metálico autoportante, instalación interior, IP 22, ejecución fija. Acceso de cables inferior. Compuesto por: Interruptor Caja moldeada, Variador de frecuencia p/motor de bomba de condensado PAZ-24210C. Lógica de comando 220/24Vca. Luces indicadoras y selectora en puerta. - 373kW - 380 Vca - 3F	1180	(15000) Stand BY
13	---	Espacio de RESERVA		
14	102-VCC-001A	Doble Rectificador / cargador de baterías, con modo de operación con redundancia en caliente, conformados con tecnología de puentes rectificadores con tecnología estática trirrectificada. Control digital con panel de visualización de variables, alarmas y estados. - 20 kW Alimentación: 380 Vac - 3F+N - Salida: 110 Vcc - P+N	850	1250
15	102-VCC-001B	Doble Rectificador / cargador de baterías, con modo de operación con redundancia en caliente, conformados con tecnología de puentes rectificadores con tecnología estática trirrectificada. Control digital con panel de visualización de variables, alarmas y estados. - 20 kW Alimentación: 380 Vac - 3F+N - Salida: 110 Vcc - P+N	850	1250
14A	102-DR-001	Dropper	450	1700
16	102-DP-001VCC	Tablero de distribución para sistema de corriente continua, autoportante. Tensión de aislamiento 1 kV. Grado de protección IP41. Grado de protección con puerta abierta IP20. Acometida-Salidas Superior/inferior. - 200 A	300	200
17	102-SDB-002	Interruptor Desconector Banco de Baterías.	100	200
18	102-BB-002A	Banco de Baterías, tecnología VRLA, para sistema de corriente continua 102-VCC-001A/B, con autonomía de 4hs - 1160Ah - 202A	2000	1500
18	102-BB-002B	Banco de Baterías, tecnología VRLA, para sistema de corriente continua 102-VCC-001A/B, con autonomía de 4hs - 1160Ah - 202A	2000	1500
19	102-UPS-001A	Doble UPS de corriente alterna, redundancia en caliente, del tipo "en línea", grado industrial de doble conversión, con generación de onda senoidal, con un sistema de by-pass (compartido por ambas UPS's) con bave de transferencia manual/automática y transformador de by-pass asociado. - 40 kVA Alimentación: 380 Vac - 3F+N Salida: 220 Vac - F+N	1200	3250
20	102-UPS-001B	Doble UPS de corriente alterna, redundancia en caliente, del tipo "en línea", grado industrial de doble conversión, con generación de onda senoidal, con un sistema de by-pass (compartido por ambas UPS's) con bave de transferencia manual/automática y transformador de by-pass asociado. - 40 kVA Alimentación: 380 Vac - 3F+N Salida: 220 Vac - F+N	1200	3250
21	102-BY-001	Tablero de distribución para sistema de UPS de corriente alterna, autoportante, montaje sobre pared. Tensión de aislamiento 1 kV. Grado de protección IP41. Grado de protección con puerta abierta IP20. Acometida-Salidas Superior/inferior - 250 A	500	500
22	102-DP-001UPS	Tablero de distribución para sistema de UPS de corriente alterna, autoportante, montaje sobre pared. Tensión de aislamiento 1 kV. Grado de protección IP41. Grado de protección con puerta abierta IP20. Acometida-Salidas Superior/inferior - 250 A	300	200
23	102-SDB-001A	Interruptor Desconector Banco de Baterías "A"	100	200
23A	102-SDB-001B	Interruptor Desconector Banco de Baterías "B"	100	200
24	102-BB-001A	Banco de Baterías, tecnología VRLA, para sistema UPS de corriente alterna 102-UPS-001A, con autonomía de 4hs - 850Ah	3200	2500
24	102-BB-001B	Banco de Baterías, tecnología VRLA, para sistema UPS de corriente alterna 102-UPS-001A, con autonomía de 4hs - 850Ah	3200	2500
24A	102-BB-001B	Banco de Baterías, tecnología VRLA, para sistema UPS de corriente alterna 102-UPS-001A, con autonomía de 4hs - 850Ah	3200	2500

25	102-DP-001-TRA	Tablero de distribución para servicios auxiliares de la Sala Eléctrica y de los tableros. Autoportante o de pared. Tensión de aislamiento 1 kV. Grado de protección IP41. Grado de protección con puerta abierta IP20. Acometida inferior. Salida de cable inferior. - 400 A - 50 kA (1s) - 380 / 220 Vca - 3F+N	200	150
26	102-LP-001	Tablero de distribución para servicios auxiliares de la Sala Eléctrica y de los tableros. Autoportante o de pared. Tensión de aislamiento 1 kV. Grado de protección IP41. Grado de protección con puerta abierta IP20. Acometida inferior. Salida de cable inferior. - 250 A - 36 kA (1s) - 380 / 220 Vca - 3F+N	300	200
27	102-LP-002	Tablero de distribución para iluminación y Tomacorrientes de Emergencia, autoportante, montaje sobre pared. Tensión de aislamiento 1 kV. Grado de protección IP41. Grado de protección con puerta abierta IP20. Acometida inferior. Salida de cable inferior. - 160 A - 50 kA (1s) - 380 / 220 Vca - 3F+N	300	150
28	102-DP-001	Tablero de distribución para servicios auxiliares de la Sala Eléctrica y de los tableros. Autoportante o de pared. Tensión de aislamiento 1 kV. Grado de protección IP41. Grado de protección con puerta abierta IP20. Acometida inferior. Salida de cable inferior. - 160 A - 36 kA (1s) - 380 / 220 Vca - 3F+N	300	200
29	102-PMS-001	Gabinetes PMS	800	250
30	---	Gabinete de Comunicaciones	75	200
31	102-CDI-001	Central Detección de Incendio	---	---
32	---	Rack de Control de Accesos y CCTV	50	50
33	---	Rack de IT provisto porterceros	50	200
34	102-HVAC-001	Tablero de distribución para sistema HVAC/Presurización/Extracción de Sala Eléctrica y Sala de Baterías, 160A - 5kA (1s) - 380/220 Vca - 3F+N	300	200
35	102-HVAC-001B	Equipos HVAC Aire Acondicionado Frío/Calor - 380Vca - 3F // 32kWf	---	---
36	102-HVAC-001A	Equipos HVAC Aire Acondicionado Frío/Calor - 380Vca - 3F // 32kWf	---	---
37	102-EXT-001	Sistema de Extracción Sala de Baterías	---	---
38	102-PRE-001	Sistema de Presurización Sala Eléctrica	---	---
39	---	Espacio de RESERVA para futura AMPLIACIÓN CCM	---	---

NOTAS:

- SE DEBERÁ GARANTIZAR UN PASO LIBRE DE 2MTS MÍNIMO MEDIDO ENTRE EL NIVEL DE TERRENO TERMINADO Y EL NIVEL INFERIOR DE LA ESTRUCTURA SOPORTE DE LA SALA.
- LAS DIMENSIONES ESTÁN EN MILÍMETROS, LAS COORDENADAS Y LOS NIVELES EN METROS.
- LAS DIMENSIONES DE LOS EQUIPOS PROVISTOS POR OTROS SON APROXIMADAS Y SERÁN DEFINIDAS DURANTE LA INGENIERÍA DE DETALLE.
- LAS DIMENSIONES EXTERIORES DE LA SALA SON ESTIMADAS Y SERÁN CONFIRMADAS CON EL AVANCE DE LA INGENIERÍA DE DETALLE.
- LAS PLATAFORMAS, ESCALERAS Y ESTRUCTURAS ASOCIADAS NO SON PROVISTAS POR ABB.
- SE CONSIDERAN 7 MÓDULOS, SI POR OPTIMIZACIÓN DE MODULARIZACIÓN Y/O TRANSPORTE SE NECESITA MODIFICAR SE PUEDE ADECUAR ESTA CANTIDAD PUDIÉNDOSE AJUSTAR LAS DIMENSIONES FINALES DE LA SALA, NUNCA EN MENOS A LAS INDICADAS.
- LA ALTURA INDICADA ES REPRESENTATIVA. SE DEFINIRÁ EN LA ETAPA DE DISEÑO EN INGENIERÍA DE DETALLE EN FUNCIÓN DE LA ALTURA INTERIOR H_{INT} INDICADA EN LISTA DE EQUIPOS.
- LAS SALAS DE TABLEROS Y BATERÍAS CONTARÁN CON SENSORES DE HIDRÓGENO, EL CUAL DARÁ ALARMA Y ACTUARÁ SOBRE EL SISTEMA HVAC PARA EL DISPARO DEL MISMO.
- LOS EJES N° 2 Y 3 INDICAN LA CORRECTA E INALTERABLE POSICIÓN DE CORTE DE LOS MÓDULOS DE LA SALA DE TABLEROS DADO QUE EN ELAS SE ENCUENTRAN LAS DIVISIONES DE LOS TABLEROS 102-CCM-005/006/007 PARA DE TRANSPORTE. DE SER NECESARIO MODIFICAR ESTAS POSICIONES SE DEBERÁ REALIZAR NUEVAMENTE EL ESTUDIO DE DIVISION.

EQUIPOS NO PROVISTOS POR ABB



COLUMNAS SOPORTES Y/U OBRA CIVIL, ESCALERAS Y PASARELAS SE
ENCUENTRAN EXCLUÍDAS DE PROVISIÓN ABB

1