




A
B
C
D
E
F

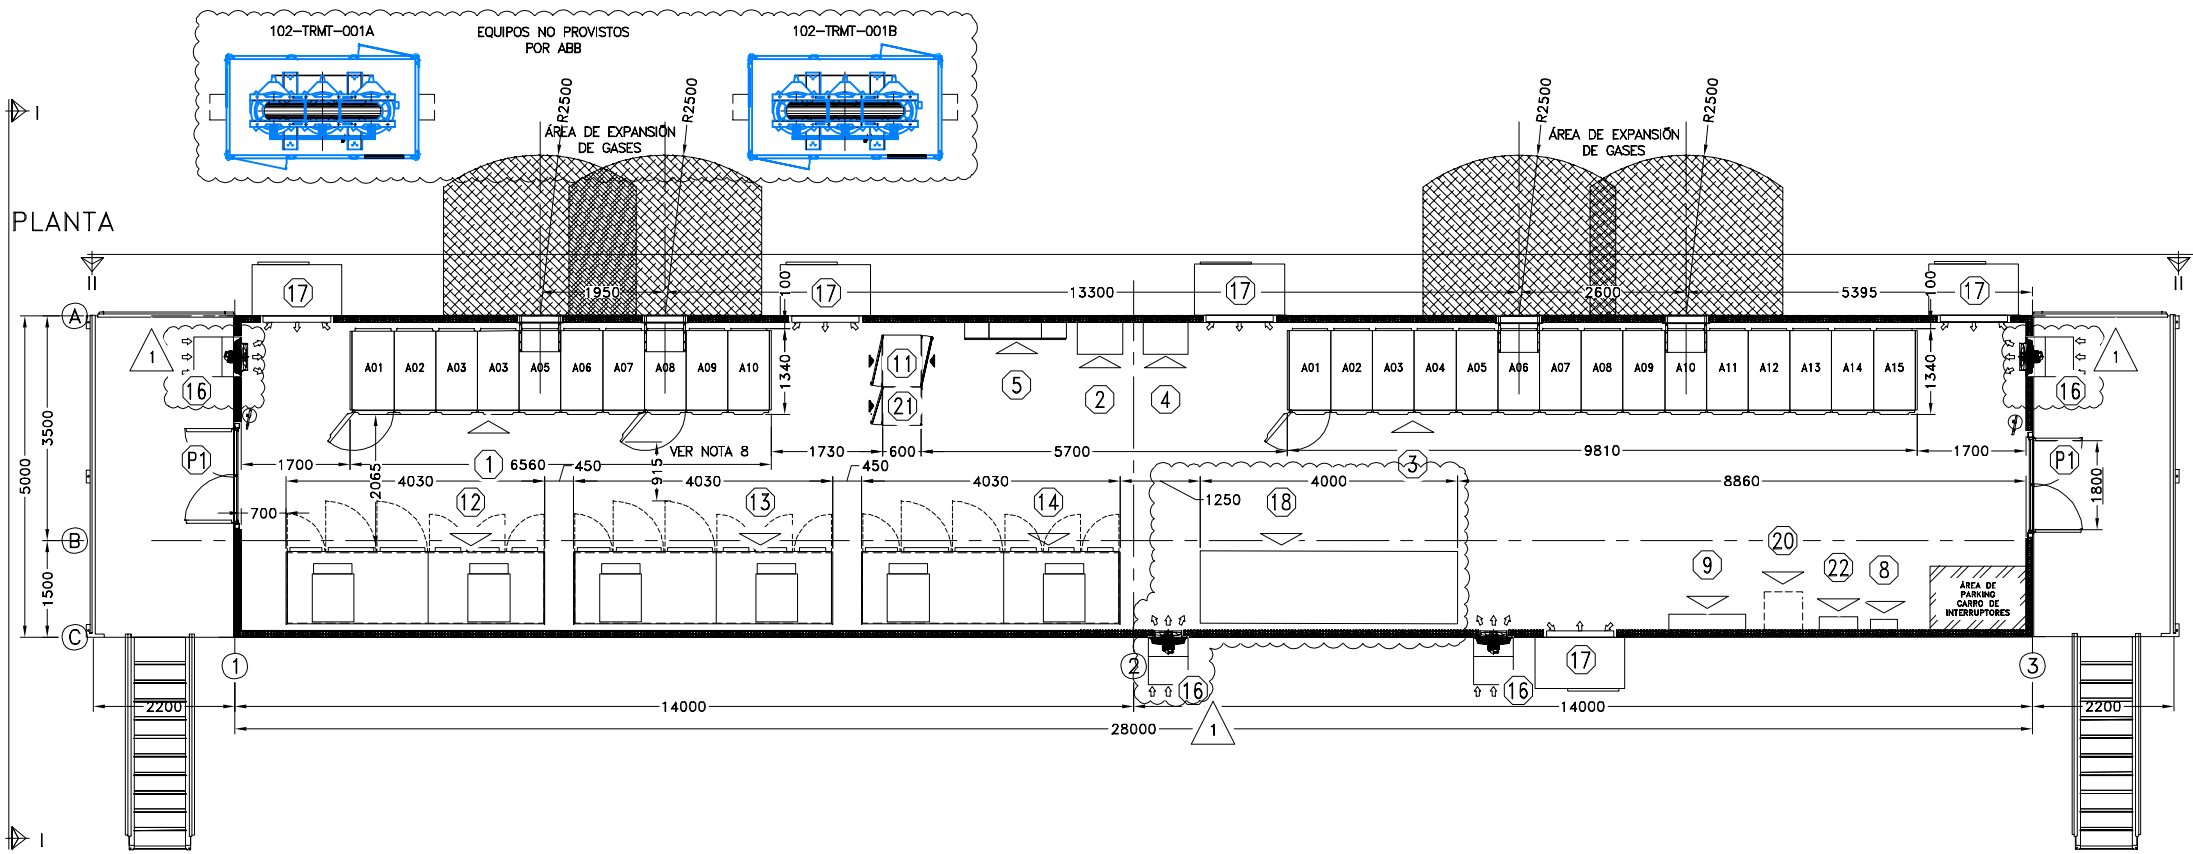

VISTA II

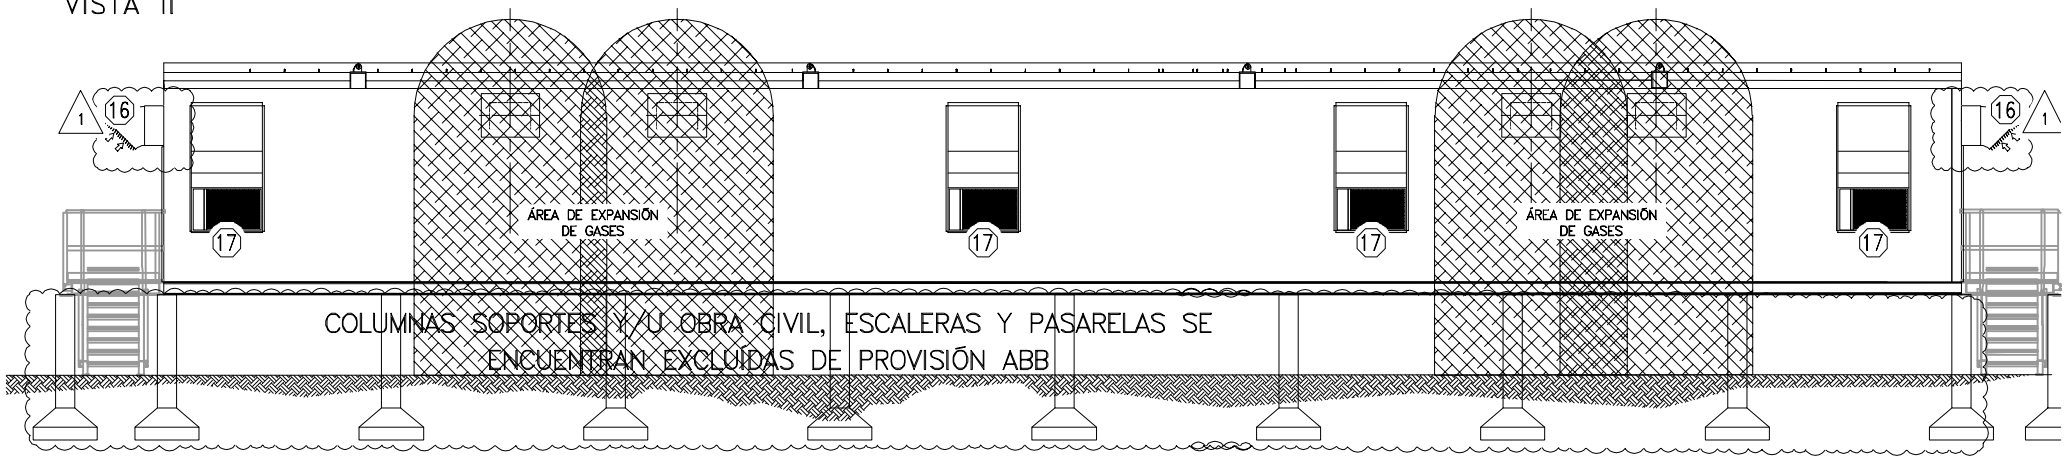

VISTA I

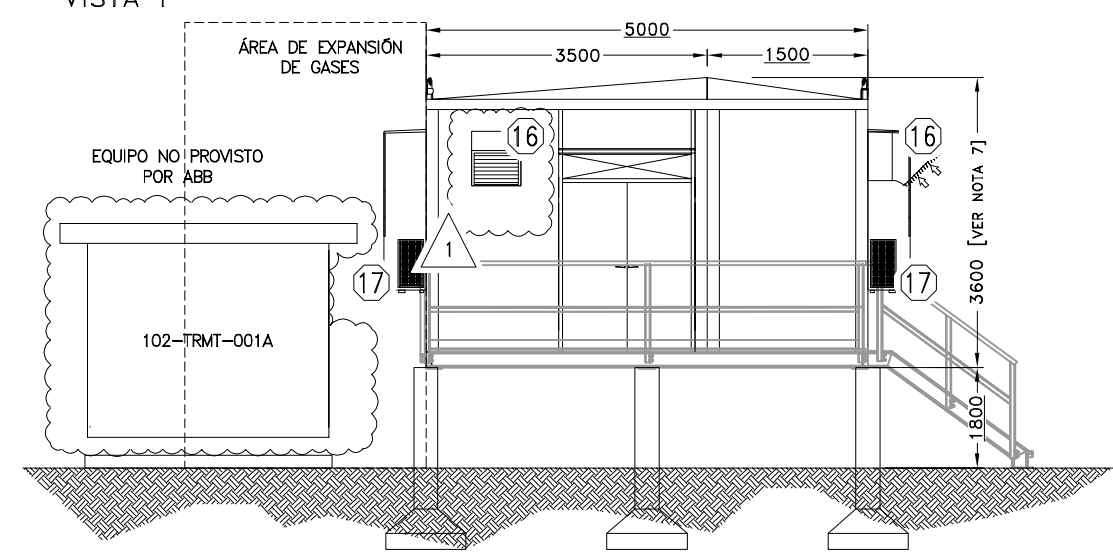

- NOTAS:
- SE DEBERÁ GARANTIZAR UN PASO LIBRE DE 2MTS MÍNIMO MEDIDO ENTRE EL NIVEL DE TERRENO TERMINADO Y EL NIVEL INFERIOR DE LA ESTRUCTURA SOPORTE DE LA SALA.
 - LAS DIMENSIONES ESTÁN EN MILÍMETROS, LAS COORDENADAS Y LOS NIVELES EN METROS.
 - LAS DIMENSIONES DE LOS EQUIPOS PROVISTOS POR OTROS SON APROXIMADAS Y SERÁN DEFINIDAS DURANTE LA INGENIERÍA DE DETALLE.
 - LAS DIMENSIONES EXTERIORES DE LA SALA SON ESTIMADAS Y SERÁN CONFIRMADAS CON EL AVANCE DE LA INGENIERÍA DE DETALLE.
 - LAS PLATAFORMAS, ESCALERAS Y ESTRUCTURAS ASOCIADAS NO SON PROVISTAS POR ABB.
 - SE CONSIDERAN 4 MÓDULOS, SI POR OPTIMIZACIÓN DE MODULARIZACIÓN Y/O TRANSPORTE SE NECESITA MODIFICAR SE PUEDE ADECUAR ESTA CANTIDAD PUDIÉNDOSE AJUSTAR LAS DIMENSIONES FINALES DE LA SALA, NUNCA EN MENOS A LAS INDICADAS.
 - LA ALTURA INDICADA ES REPRESENTATIVA, SE DEFINIRÁ EN LA ETAPA DE DISEÑO EN INGENIERÍA DE DETALLE EN FUNCIÓN DE LA ALTURA INTERIOR HINT INDICADA EN LISTA DE EQUIPOS.
 - LA DISTANCIA MÍNIMA DE PASILLO DE EVACUACIÓN ENTRE FRENTE DE EQUIPOS CON PUERTAS ABIERTAS O DE UN EQUIPO CON PUERTA ABIERTA Y PARED (DONDE LA PUERTA ABIERTA ESTÁ EN SU MÁXIMO GRADO DE APERTURA) ES DE 500 mm DE ACUERDO A LA NORMA IEC 60364-7-729.

LISTA DE EQUIPOS A PROVEER ABB					
REF.	TAG	DESCRIPCIÓN	PESO [kg]	DISIPACIÓN [kW]	
---	SE #4	Sala Eléctrica Modular, dimensiones estimadas en mts, L= 28,0 x A= 5,0 x H=3,5	---	---	
P1	---	Portón de Acceso de Equipos/Personal, ancho libre 1400mm (2 hojas, 900mm + 500mm) x alto libre 2100mm + paño removible de 600mm quedando una altura libre total de 2700mm	---	---	
1	102-TGMT-003	SWG 6,6kV - 50Hz - 25kA/1s - 630A	9140	10000	
2	102-DP-101UPS	Tablero de distribución para sistema de UPS - 63A - 16kA - 220Vca - P+N	300	500	
3	102-TGMT-001	SWG 13,2kV - 50Hz - 25kA/1s - 630A	13860	15000	
4	102-DP-101VCC	Tablero de distribución para sistema de corriente continua - 80A - 16kA - 110Vcc - P+N	200	500	
5	102-DP-101	Tablero de distribución para servicios auxiliares para tableros 380/220Vca - 160A - 36kA - 3F+N	300	1000	
6	---	---	---	---	
8	102-CDI-201	Central Detección de Incendio	---	---	
9	102-DP-201	Tablero de distribución para sistema HVAC/Presurización/Extracción de Sala Eléctrica y Sala de Batenías, 160A - 5kA (1s) - 380/220 Vca - 3F+N	200	500	
11	102-PMS-003	Gabinete PMS	---	---	
12	102-DP-VFD-23310A	Tablero metálico autoportante, instalación interior, IP 22, ejecución fija. Acceso de cables inferior. Compuesto por: Variador de frecuencia p/motor de bomba de condensado. Lógica de comando 220/24Vca. Luces indicadores y selector en puerta. - 600kV - 6,6kV	4300	29000	
13	102-DP-VFD-23310B	Tablero metálico autoportante, instalación interior, IP 22, ejecución fija. Acceso de cables inferior. Compuesto por: Variador de frecuencia p/motor de bomba de condensado. Lógica de comando 220/24Vca. Luces indicadores y selector en puerta. - 600kV - 6,6kV	4300	29000	
14	102-DP-VFD-23310C	Tablero metálico autoportante, instalación interior, IP 22, ejecución fija. Acceso de cables inferior. Compuesto por: Variador de frecuencia p/motor de bomba de condensado. Lógica de comando 220/24Vca. Luces indicadores y selector en puerta. - 600kV - 6,6kV	4300	0 - [SPARE]	
15	---	---	---	---	
16	102-PRE-201	Sistema de Presurización Sala Eléctrica	---	---	
17	102-HVAC-201	Equipos HVAC Aire Acondicionado Frio/Calor - 380Vca - 3F - Westric AM-010.	---	---	
18	---	ESPACIO RESERVA PARA FUTURO 102-DP-VFD-23310D	---	---	
19	---	---	---	---	
20	---	Rack de IT provisto por terceros	50	200	
21	---	Gabinete de Comunicaciones	75	200	
22	---	Rack de Control de Accesos y CCTV	50	50	