


SHELTER INS-007

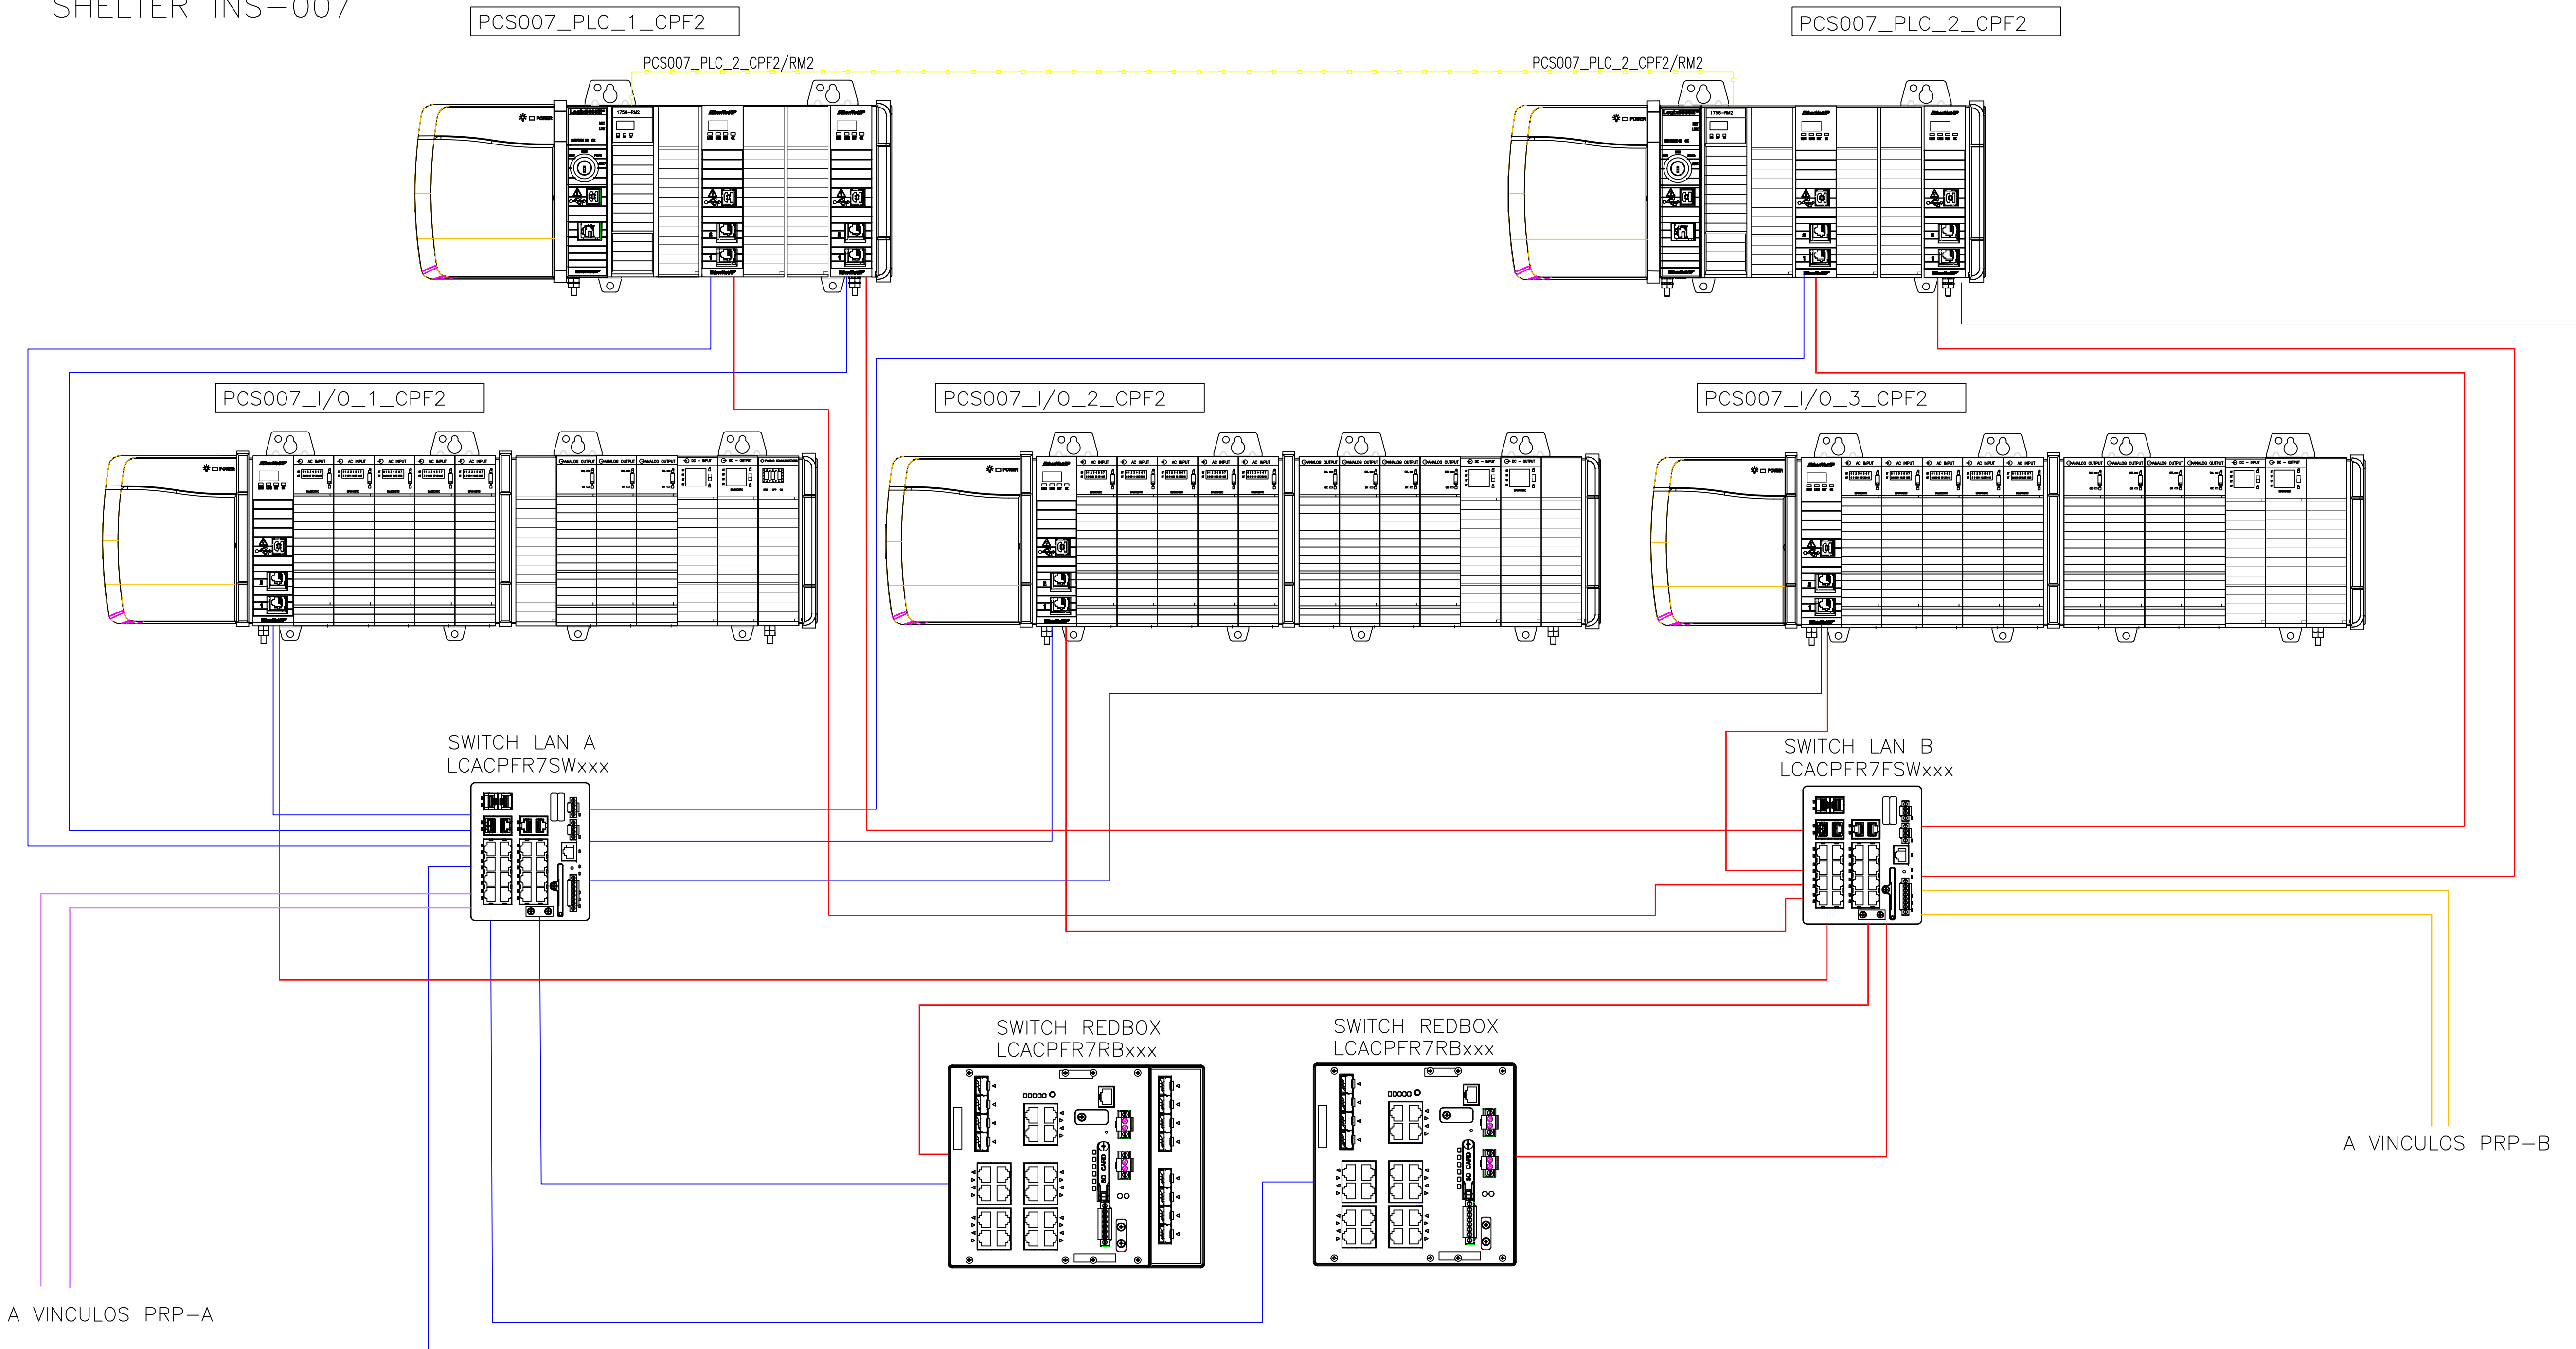

REFERENCIAS

	COMUNICACION FIBRA OPTICA MONOMODO LAN A
	COMUNICACION FIBRA OPTICA MONOMODO LAN B
	COMUNICACION FTP EQUIPOS
	COMUNICACION FIBRA OPTICA EQUIPOS
	COMUNICACION FIBRA OPTICA REDUNDANCIA
	COMUNICACION PCS LAN A
	COMUNICACION PCS LAN B

REV.	DESCRIPTION	FECHA	POR	CH.	APP.
PROYECTO: CENTRAL PRODUCTION FACILITIES - CNQ26 LA CALERA					
TITULO: ARQUITECTURA DE SISTEMAS PCS					
FACILITIES ENGINEERING & CONSTRUCTION					
Toda la información contenida en este documento es confidencial y propiedad de Pluspetrol, la reproducción o copia total o parcial del mismo está prohibida sin previa autorización.					
ESCALA	DOCUMENTO N°:	ACAL-100-PL-K-100		REVISION	13
S/E	REEMPLAZA:			PAGINA:	3 DE 3